PROJETO EXECUTIVO

PROPRIETÁRIO: VICTOR GABRIEL PINTO GUEDES
EDIFÍCIO: ESSENTIAL PERDIZES BY ONE
UNIDADE: 313
ENDEREÇO: RUA IPEROIG, 180, PERDIZES, SÃO PAULO - SP

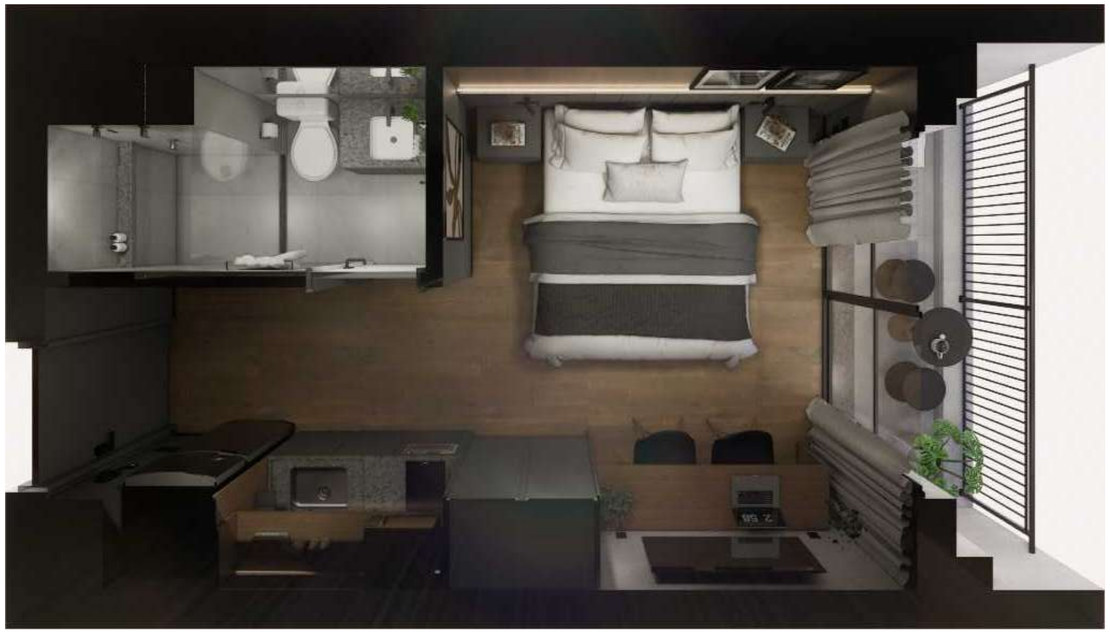

TODAS AS MEDIDAS DEVEM SER CONFERIDAS NO LOCAL E SÃO DE RESPONSÁBILIDADE DO FORNECEDOR CONTRATADO

RESPONSÁVEL TÉCNICO: ARQUITETO THIAGO DANTAS DO AMOR - CAU A162437-7

EXECUTIVO	PROPRIETÁRIO: VICTOR GABRIEL PINTO GUEDES		CONTEÚDO:	CAPA
	ARQUITETO: GUILHERME F.	DATA: 29/08/2025	REVISÃO: 03	FOLHA: 01/16

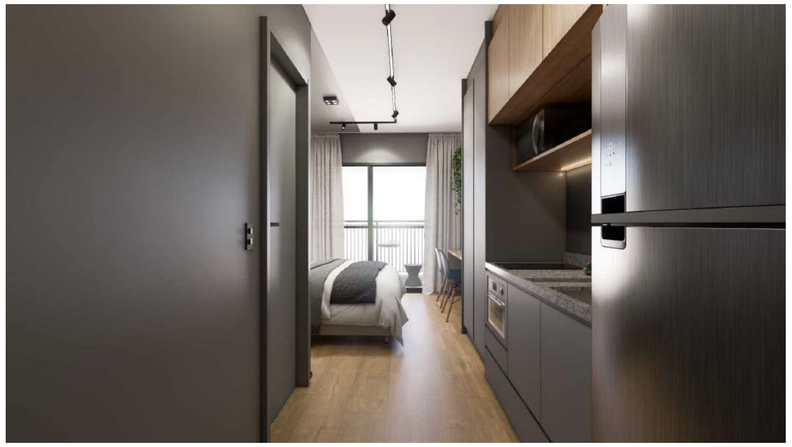

TODAS AS MEDIDAS DEVEM SER CONFERIDAS NO LOCAL E SÃO DE RESPONSÁBILIDADE DO FORNECEDOR CONTRATADO

RESPONSÁVEL TÉCNICO: ARQUITETO THIAGO DANTAS DO AMOR - CAU A162437-7

Bwild	EXECUTIVO	PROPRIETÁRIO: VICTOR GABRIEL PINTO GUEDES		CONTEÚDO: IMAGENS 3D	
		ARQUITETO: GUILHERME F.	DATA: 29/08/2025	REVISÃO: 03	FOLHA: 02/16

TODAS AS MEDIDAS DEVEM SER CONFERIDAS NO LOCAL E SÃO DE RESPONSÁBILIDADE DO FORNECEDOR CONTRATADO

RESPONSÁVEL TÉCNICO: ARQUITETO THIAGO DANTAS DO AMOR - CAU A162437-7

Bwild	EXECUTIVO	PROPRIETÁRIO: VICTOR GABRIEL PINTO GUEDES		CONTEÚDO: IMAGENS 3D	
		ARQUITETO: GUILHERME F.	DATA: 29/08/2025	REVISÃO: 03	FOLHA: 03/16

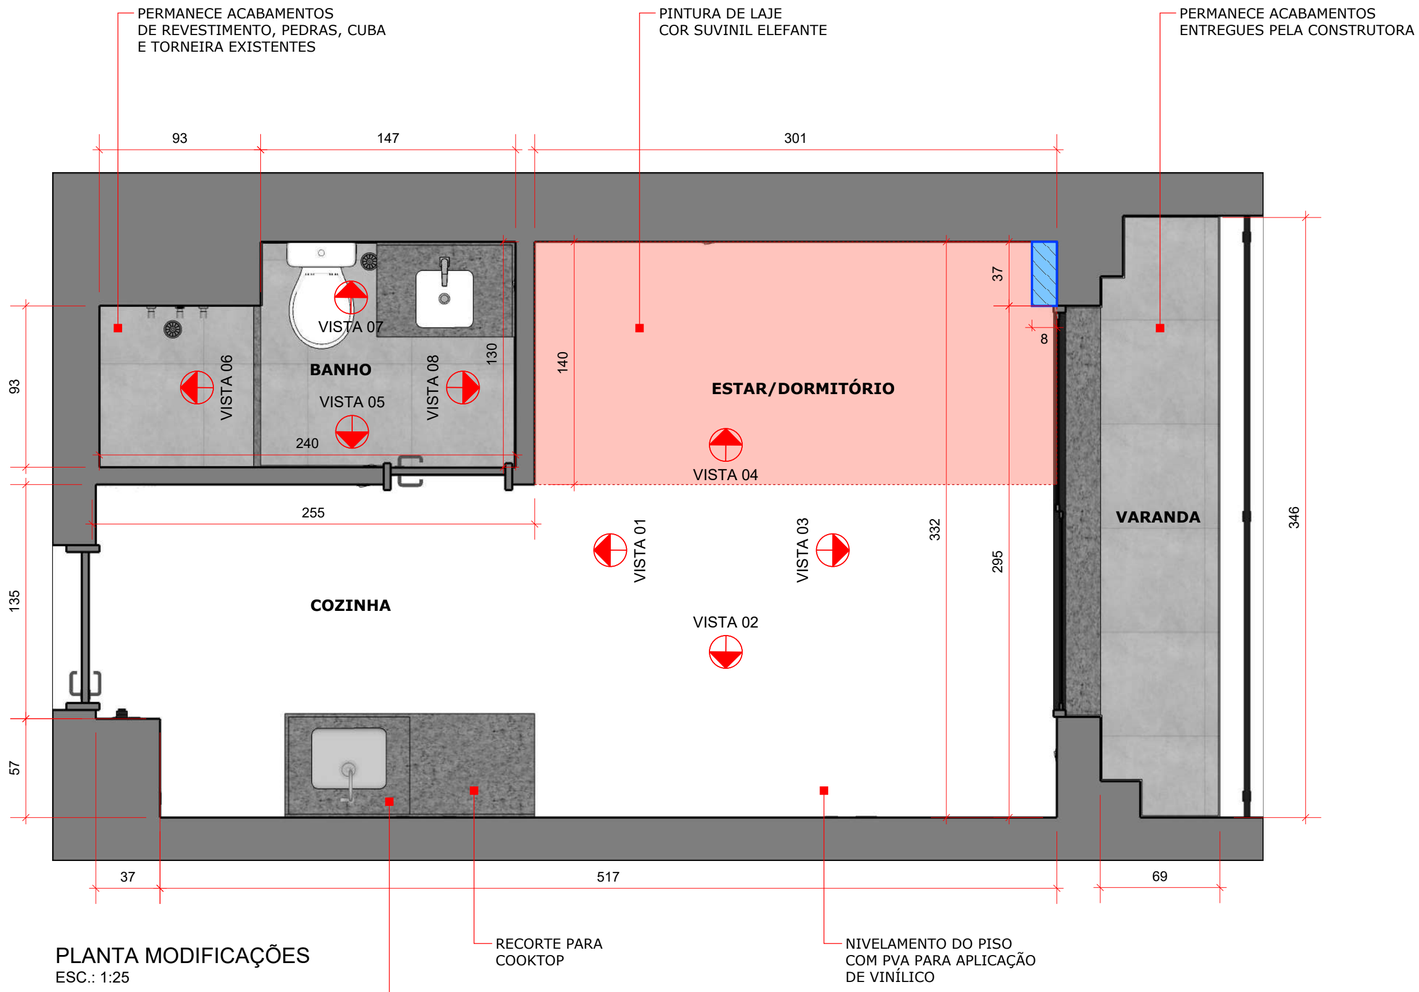

PLANTA MODIFICAÇÕES
ESC.: 1:25

LEGENDA:

CONSTRUIR - DRYWALL

TODAS AS MEDIDAS DEVEM SER CONFERIDAS NO LOCAL E SÃO DE RESPONSÁBILIDADE DO FORNECEDOR CONTRATADO

RESPONSÁVEL TÉCNICO: ARQUITETO THIAGO DANTAS DO AMOR - CAU A162437-7

Bwild	EXECUTIVO	PROPRIETÁRIO: VICTOR GABRIEL PINTO GUEDES		CONTEÚDO: MODIFICAÇÕES
		ARQUITETO: GUILHERME F.	DATA: 29/08/2025	REVISÃO: 03	FOLHA: 04/16

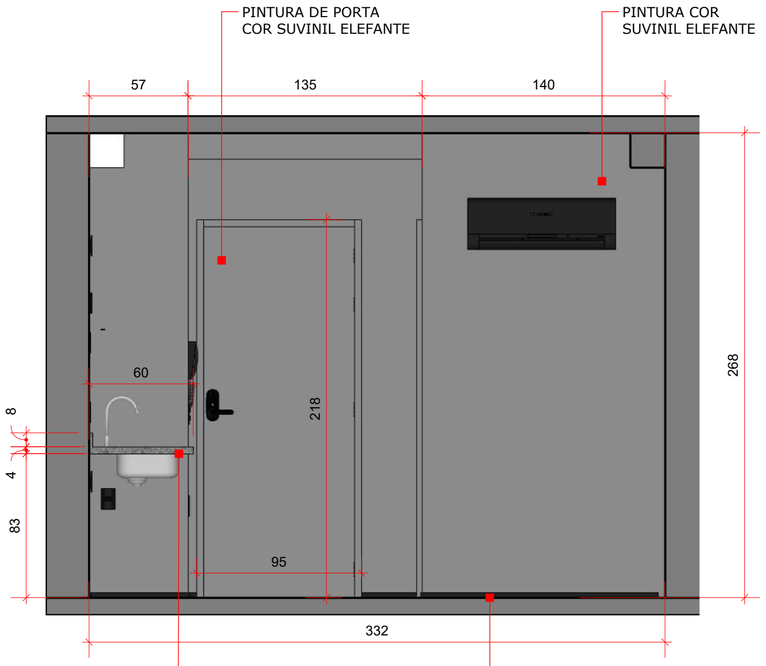

VISTA 01
ESC.: 1:25

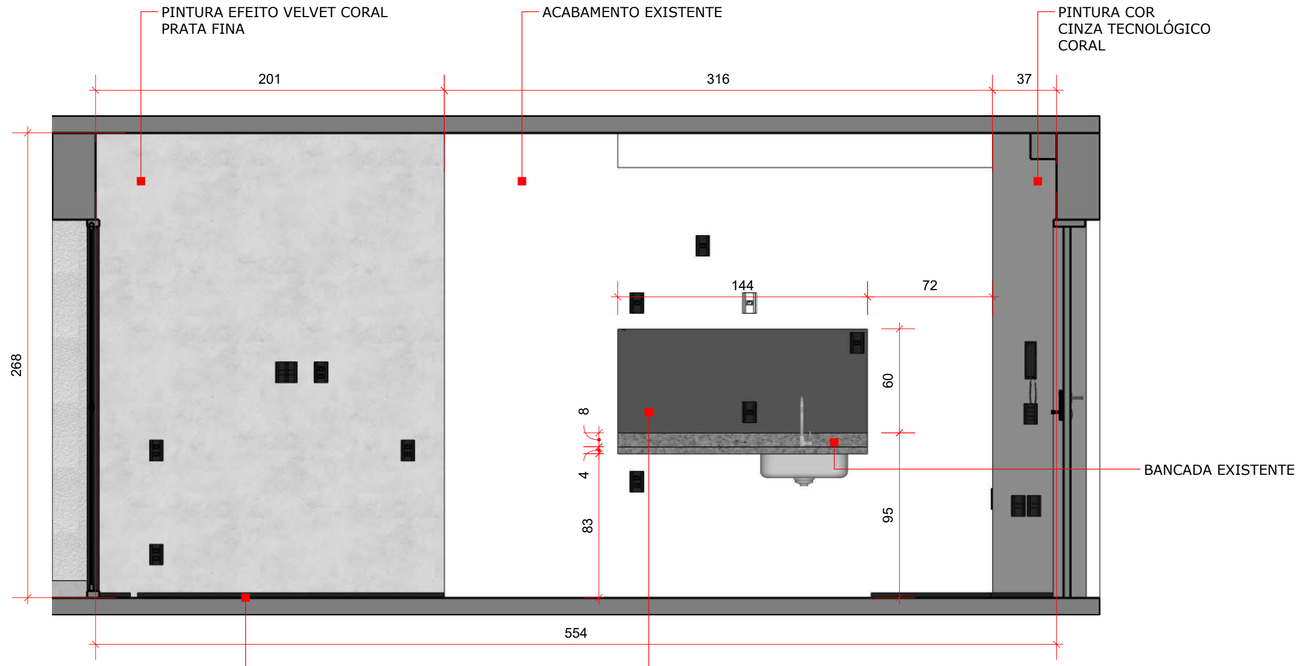

VISTA 02
ESC.: 1:25

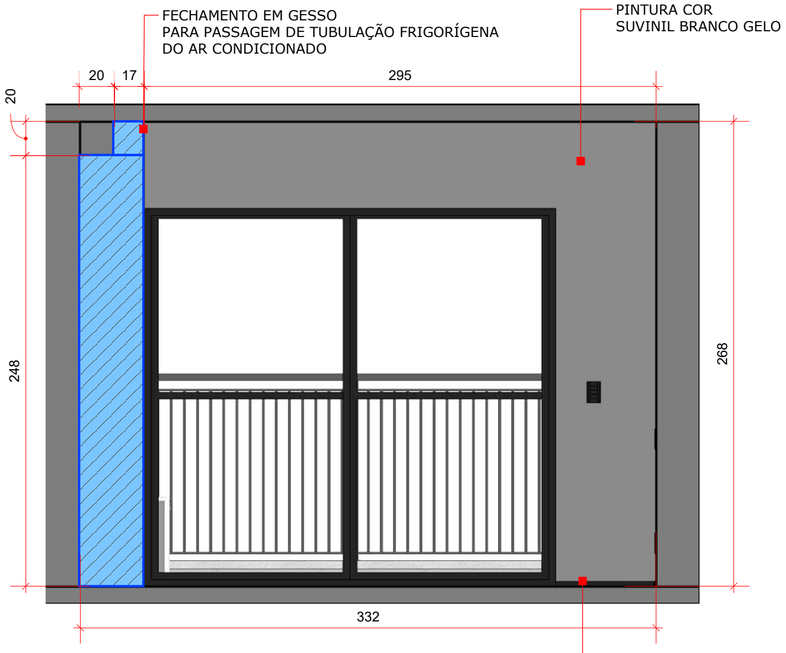

VISTA 03
ESC.: 1:25

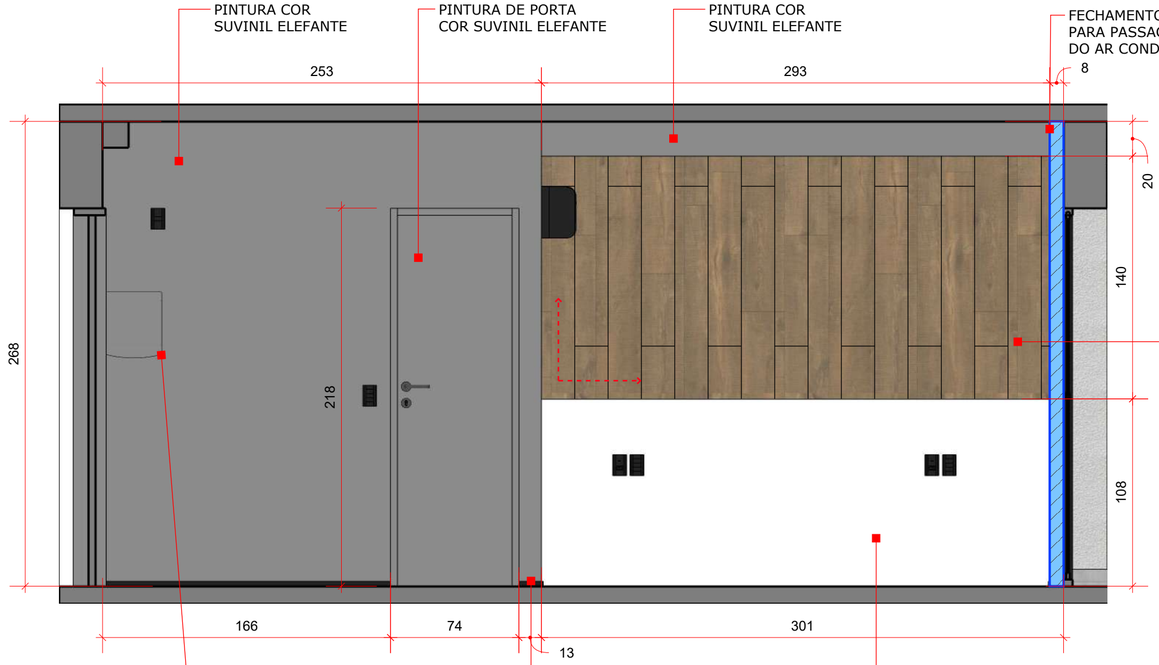

VISTA 04
ESC.: 1:25

APLICAÇÃO DO VINÍLICO
NA PAREDE PARA CABECEIRA

BIANCOGRES
VINÍLICO VITA TREVI
130X19CM
A: 4,10m² SEM QUEBRA

INDICAÇÃO DO INÍCIO DA
PAGINAÇÃO

LEGENDA:

CONSTRUIR - DRYWALL

TODAS AS MEDIDAS DEVEM SER CONFERIDAS NO LOCAL E SÃO DE RESPONSÁBILIDADE DO FORNECEDOR CONTRATAD

RESPONSÁVEL TÉCNICO: ARQUITETO THIAGO DANTAS DO AMOR - CAU A162437-7

Bwild	EXECUTIVO	PROPRIETÁRIO: VICTOR GABRIEL PINTO GUEDES		CONTEÚDO: VISTAS MODIFICAÇÕES	
		ARQUITETO: GUILHERME F.	DATA: 29/08/2025	REVISÃO: 03	FOLHA: 05/16

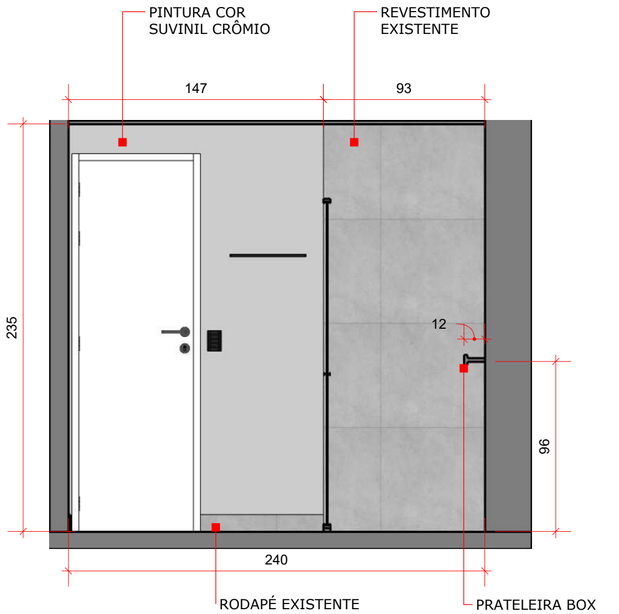

VISTA 05
ESC.: 1:25

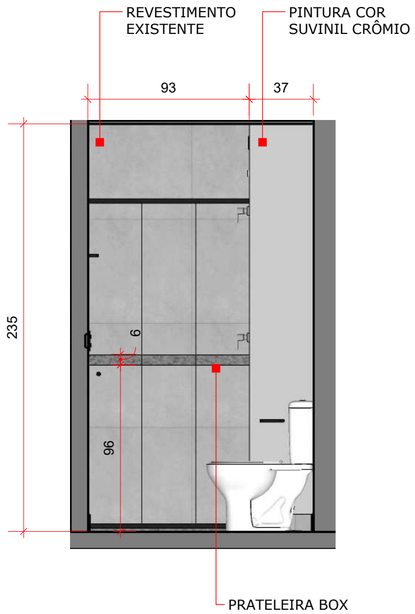

VISTA 06
ESC.: 1:25

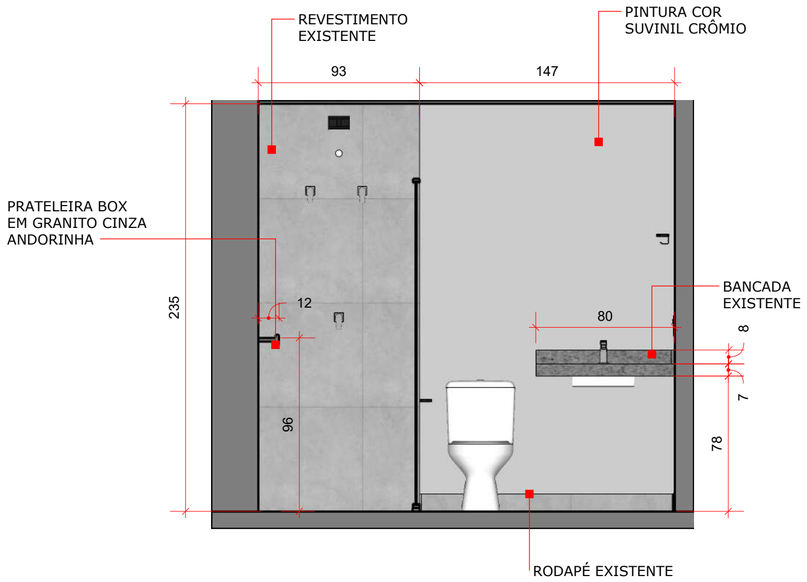

VISTA 07
ESC.: 1:25

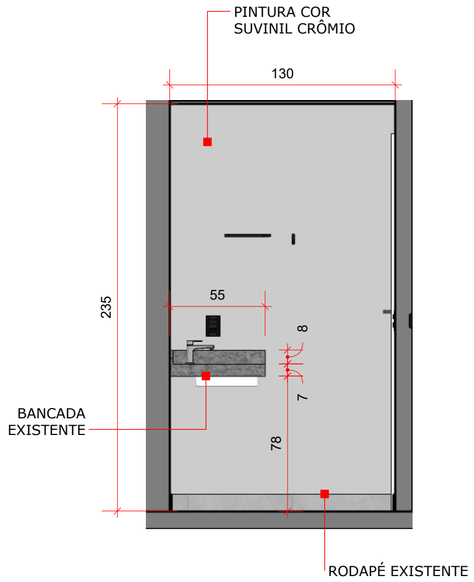

VISTA 08
ESC.: 1:25

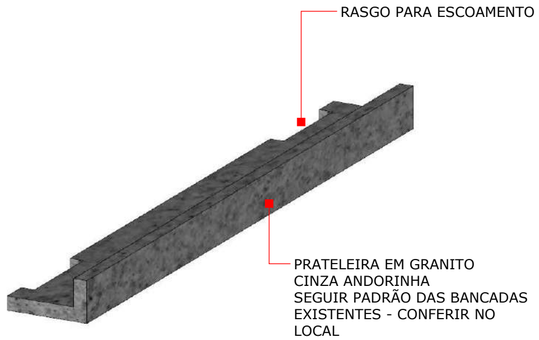

PERSPECTIVA - PRATELEIRA BOX

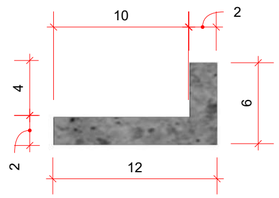

VISTA LATERAL - PRATELEIRA BOX

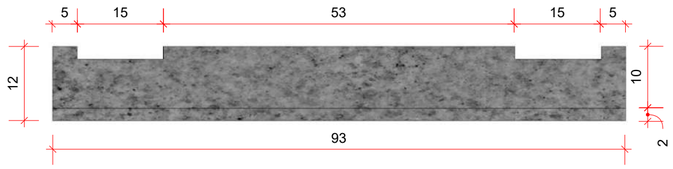

PLANTA BAIXA - PRATELEIRA BOX

TODAS AS MEDIDAS DEVEM SER CONFERIDAS NO LOCAL E SÃO DE RESPONSÁBILIDADE DO FORNECEDOR CONTRATADO

RESPONSÁVEL TÉCNICO: ARQUITETO THIAGO DANTAS DO AMOR - CAU A162437-7

Bwild	EXECUTIVO	PROPRIETÁRIO: VICTOR GABRIEL PINTO GUEDES		CONTEÚDO: VISTAS MODIFICAÇÕES	
		ARQUITETO: GUILHERME F.	DATA: 29/08/2025	REVISÃO: 03	FOLHA: 06/16

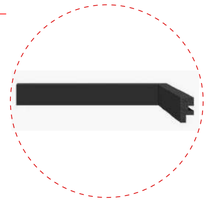

APLICAÇÃO DO RODAPÉ APÓS A INSTALAÇÃO DA MARCENARIA

RODAPÉ EM POLIESTIRENO PRETO
ALTURA: 3cm
METRAGEM LINEAR: 7,60m

INDICAÇÃO DA APLICAÇÃO DO RODAPÉ

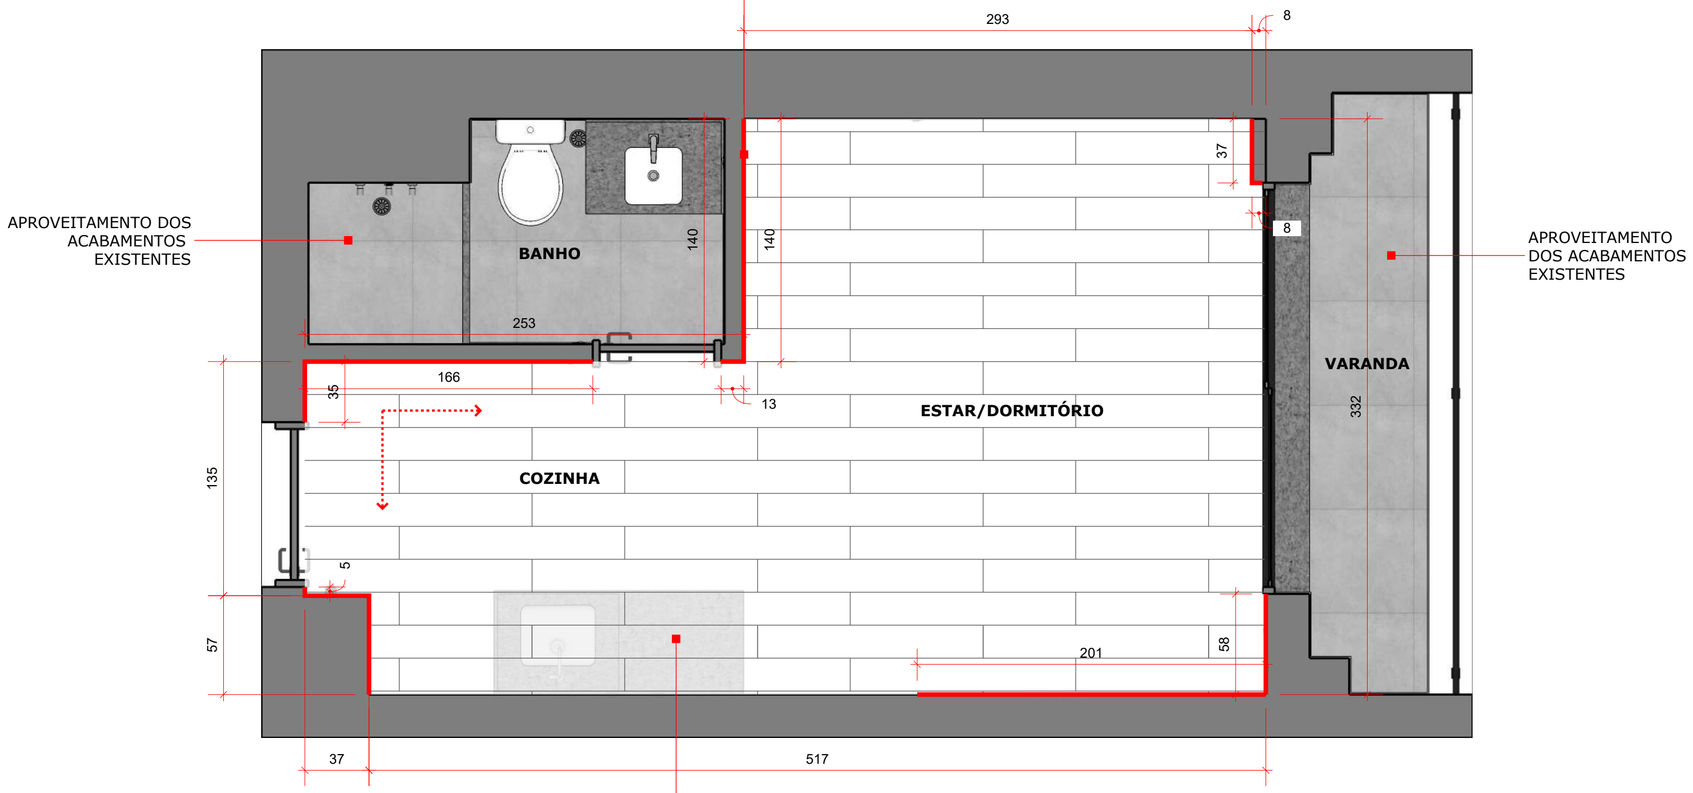

PLANTA ACABAMENTOS
ESC.: 1:25

APLICAÇÃO DO VINÍLICO SOBRE NIVELAMENTO PVA

BIANCOGRES
VINÍLICO VITA TREVI
130X19CM
A: 14,70m² SEM QUEBRA

INDICAÇÃO DO INÍCIO DA PAGINAÇÃO

TODAS AS MEDIDAS DEVEM SER CONFERIDAS NO LOCAL E SÃO DE RESPONSÁBILIDADE DO FORNECEDOR CONTRATADO

RESPONSÁVEL TÉCNICO: ARQUITETO THIAGO DANTAS DO AMOR - CAU A162437-7

Bwild	EXECUTIVO	PROPRIETÁRIO: VICTOR GABRIEL PINTO GUEDES		CONTEÚDO: PLANTA ACABAMENTOS	
		ARQUITETO: GUILHERME F.	DATA: 29/08/2025	REVISÃO: 03	FOLHA: 07/16

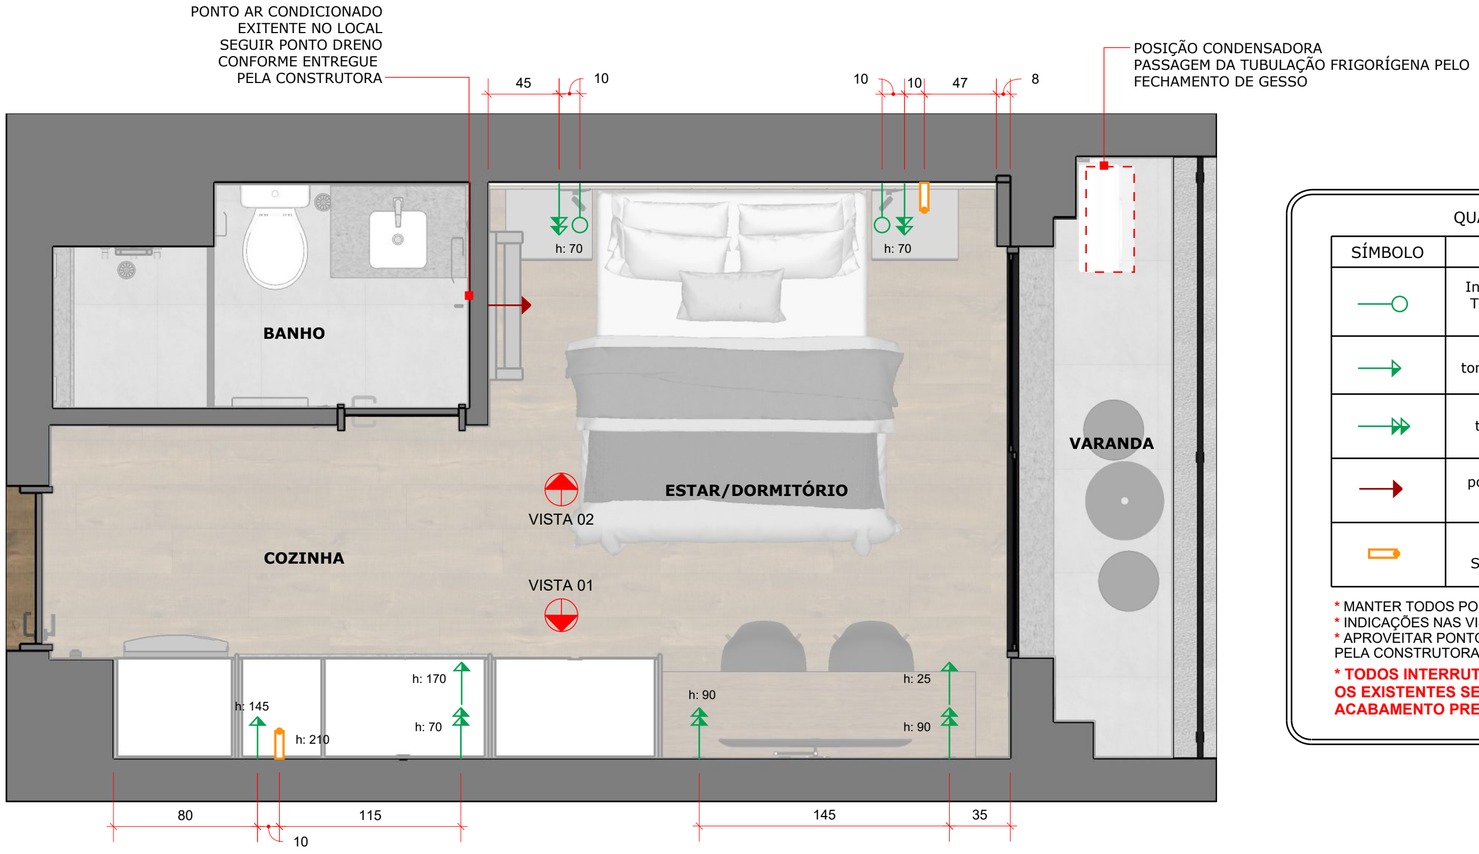

PLANTA ELÉTRICA
ESC.: 1:25

QUADRO DE TOMADAS

SÍMBOLO	DESCRIÇÃO	QUANT.
	Interruptor duplo + Tomada individual 2P+T	02
	tomada individual 2p+T	03
	tomada dupla 2p+T	05
	ponto ar condicionado existente no local	01
	Ponto LED Somente eletrotudo	02

* MANTER TODOS PONTOS ELÉTRICOS EXISTENTES
* INDICAÇÕES NAS VISTAS
* APROVEITAR PONTOS AR CONDICIONADO ENTREGUES PELA CONSTRUTORA

*** TODOS INTERRUTORES E TOMADAS, INCLUSIVE OS EXISTENTES SERÃO TROCADOS PARA ACABAMENTO PRETO BLUX**

TODAS AS MEDIDAS DEVEM SER CONFERIDAS NO LOCAL E SÃO DE RESPONSÁBILIDADE DO FORNECEDOR CONTRATADO

RESPONSÁVEL TÉCNICO: ARQUITETO THIAGO DANTAS DO AMOR - CAU A162437-7

Bwild	EXECUTIVO	PROPRIETÁRIO: VICTOR GABRIEL PINTO GUEDES		CONTEÚDO: PLANTA ELÉTRICA	
		ARQUITETO: GUILHERME F.	DATA: 29/08/2025	REVISÃO: 03	FOLHA: 08/16

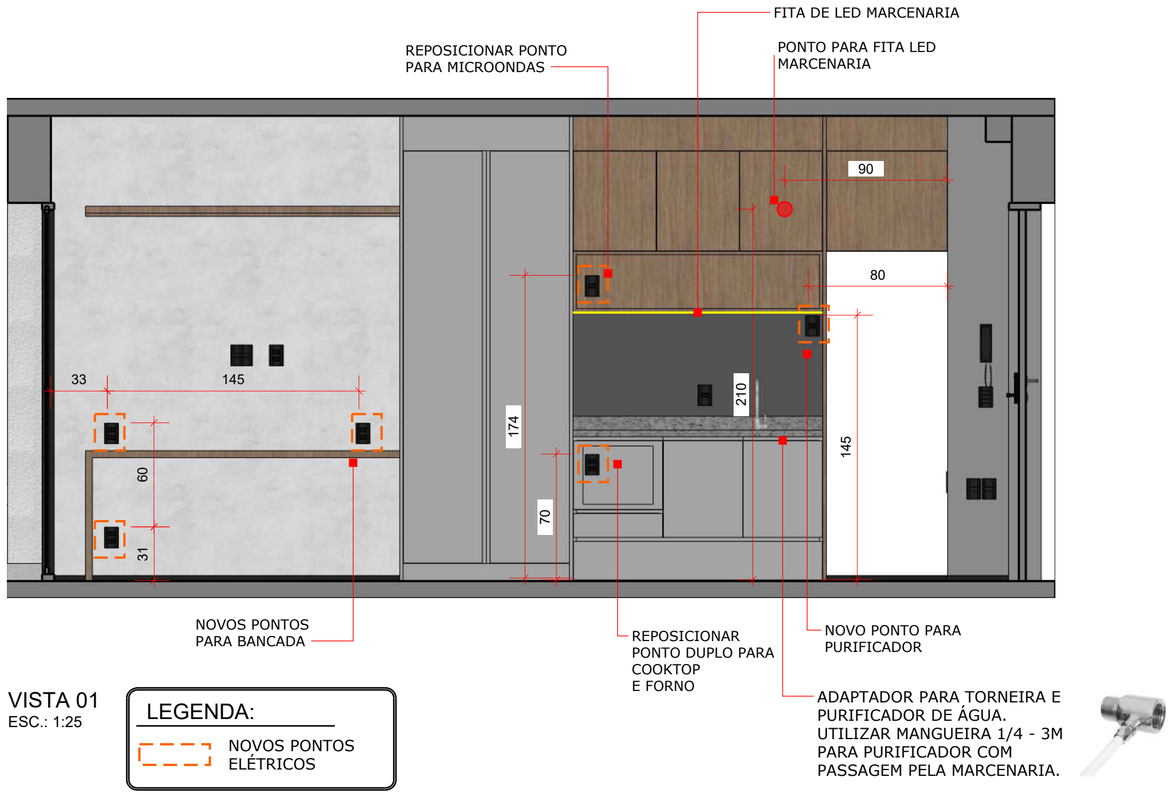

VISTA 01
ESC.: 1:25

LEGENDA:
NOVOS PONTOS ELÉTRICOS

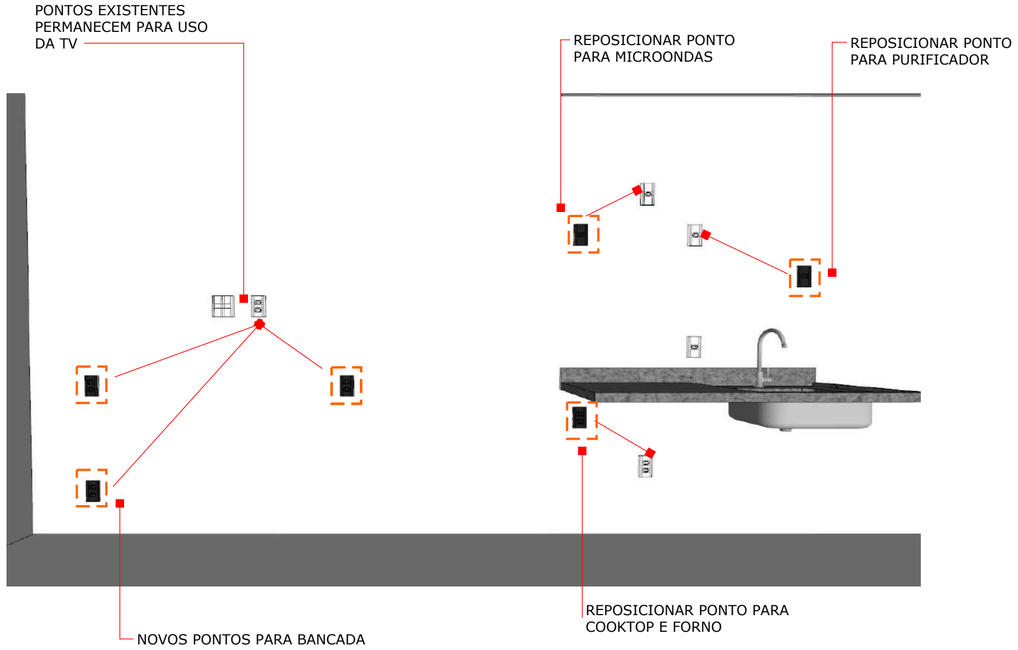

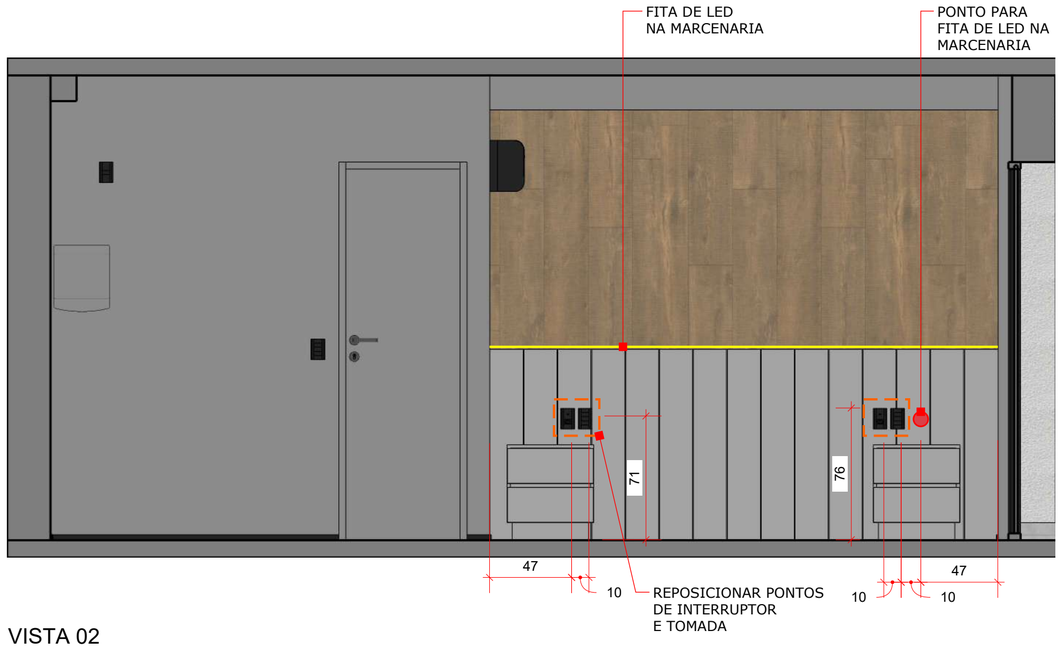

VISTA 02
ESC.: 1:25

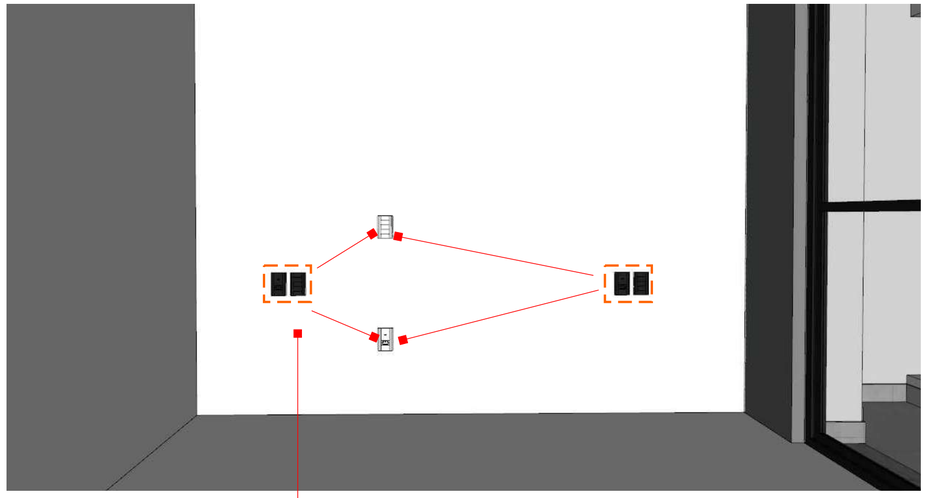

TODAS AS MEDIDAS DEVEM SER CONFERIDAS NO LOCAL E SÃO DE RESPONSÁBILIDADE DO FORNECEDOR CONTRATADO

RESPONSÁVEL TÉCNICO: ARQUITETO THIAGO DANTAS DO AMOR - CAU A162437-7

Bwild	EXECUTIVO	PROPRIETÁRIO: VICTOR GABRIEL PINTO GUEDES		CONTEÚDO: VISTAS ELÉTRICA	
		ARQUITETO: GUILHERME F.	DATA: 29/08/2025	REVISÃO: 03	FOLHA: 09/16

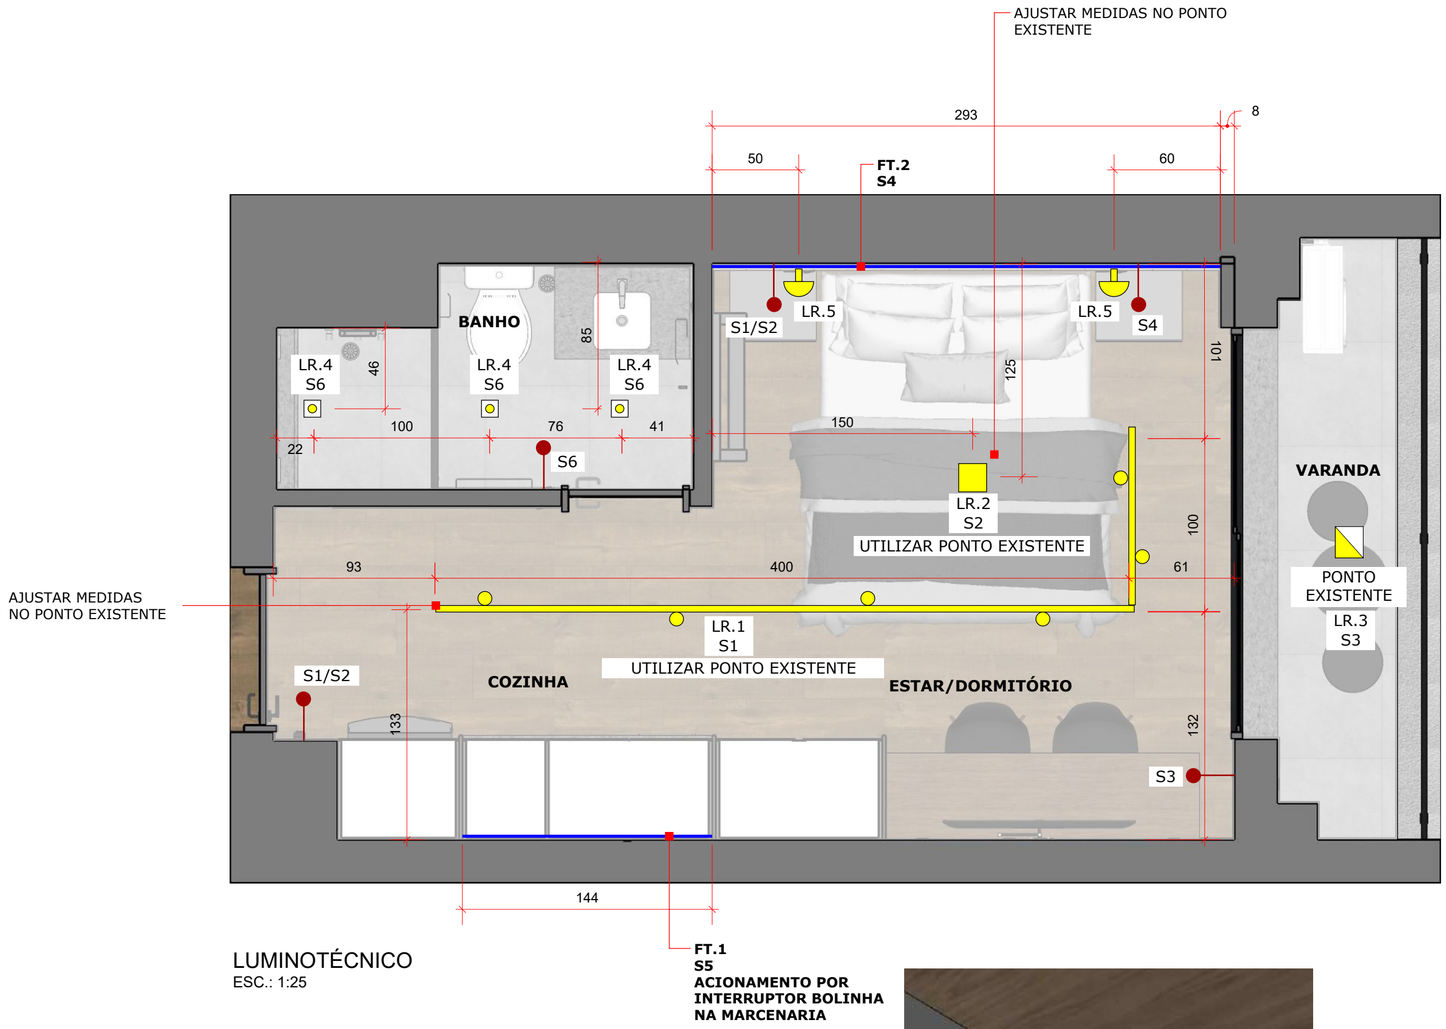

LUMINOTÉCNICO
ESC.: 1:25

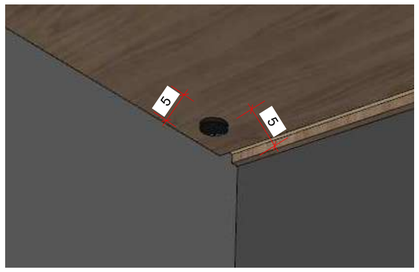

QUADRO DE LUMINÁRIAS

NOME	SÍMBOLO	DESCRIÇÃO	QUANT.
LR.1		PERFIL LED SOBREPOR PRETO COM 4 SPOTS PAR20 6K 3000K + FITA LED COB 20W/M 3000K	01 - 4M 01 - 1M
LR.2		SPOT SOBREPOR PRETO PARA 4 PAR20 5W 3000K	01
LR.3		PONTO E LUMINÁRIA EXISTENTES	01
LR.4		SPOT DE EMBUTIR PRETO PARA PAR20 6W 3000K	03
LR.5		KIT 2 ARANDELA MAGNÉTICA PRETO LED 4W 3000K 8X6,5X3CM	02
FT.1		FITA DE LED 5W/M 3000K	144cm linear
FT.2		FITA DE LED 5W/M 3000K	293cm linear

OBS.: ARANDELAS SÃO REGARREGÁVEIS E COM ACIONAMENTO NO MODELO, SEM NESSECIDADE DE ALIMENTAÇÃO ELÉTRICA.

TODAS AS MEDIDAS DEVEM SER CONFERIDAS NO LOCAL E SÃO DE RESPONSÁBILIDADE DO FORNECEDOR CONTRATADO

RESPONSÁVEL TÉCNICO: ARQUITETO THIAGO DANTAS DO AMOR - CAU A162437-7

Bwild	EXECUTIVO	PROPRIETÁRIO: VICTOR GABRIEL PINTO GUEDES		CONTEÚDO: LUMINOTÉCNICO
		ARQUITETO: GUILHERME F.	DATA: 29/08/2025	REVISÃO: 03 / FOLHA: 10/16

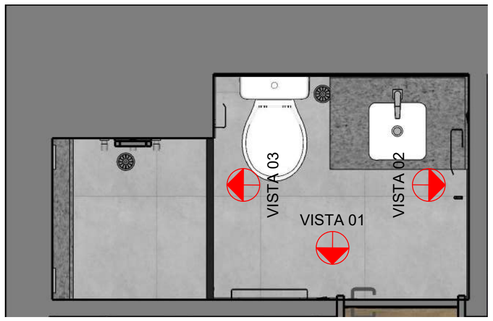

LAYOUT BANHEIRO
ESC.: 1:20

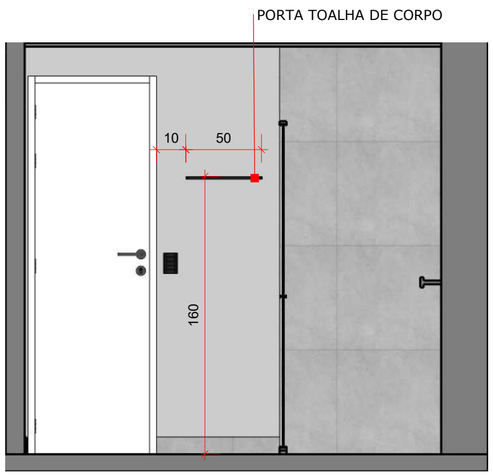

VISTA 01
ESC.: 1:25

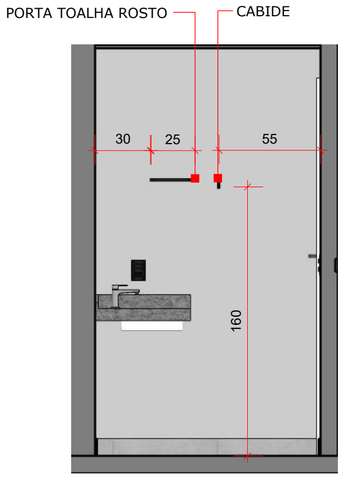

VISTA 02
ESC.: 1:25

VISTA 03
ESC.: 1:25

ASSENTO SANITÁRIO SLOW
CLOSE

CHUVEIRO LORENZETTI
ACQUA ULTRA DUO PRETO
CROMADO

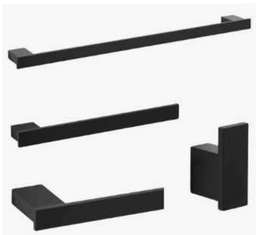

KIT DE ACESSÓRIOS PARA
BANHEIROS
PRETO MASTER
4 PEÇAS

TODAS AS MEDIDAS DEVEM SER CONFERIDAS NO LOCAL E SÃO DE RESPONSÁBILIDADE DO FORNECEDOR CONTRATADO

RESPONSÁVEL TÉCNICO: ARQUITETO THIAGO DANTAS DO AMOR - CAU A162437-7

Bwild	EXECUTIVO	PROPRIETÁRIO: VICTOR GABRIEL PINTO GUEDES		CONTEÚDO: METAIS E ACESSÓRIOS BANHEIRO
		ARQUITETO: GUILHERME F.	DATA: 29/08/2025	REVISÃO: 03 / FOLHA: 11/16

AR CONDICIONADO
9000 BTUS
INVERTER - QUENTE/FRIO
220V - ACABAMENTO PRETO

CAMA BOX BAÚ CASAL +
COLCHÃO CASAL CASAL
138X188CM -
COM CAMA DE SOLTEIRO
AUXILIAR

COMPOSIÇÃO QUADROS
DECORATIVOS
PRETO E BRANCO
02 UNIDADES - 70X50CM
01 UNIDADE - 110X80CM

GELADEIRA FROST FREE
310L
DUPLEX
INOX
VERIFICAR ESPAÇO
MARCENARIA
POR CONTA DO CLIENTE

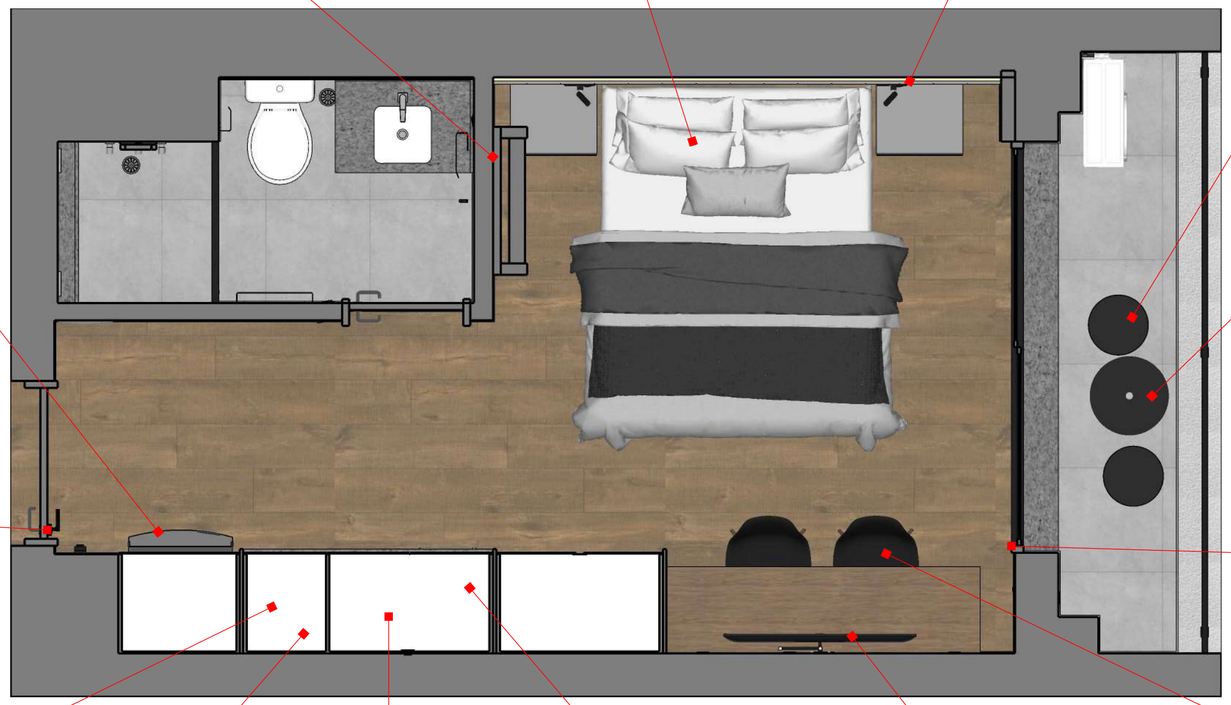

BANQUETA BAIXA
POLIPROPILENO SEM
ENCOSTO SILI PRETO
02 UNIDADES

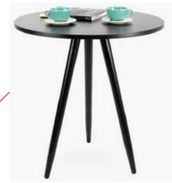

MESA REDONDA P/
ÁREA EXTERNA 50X75CM

FECHADURA DIGITAL 410S
COM ABERTURA REMOTA
VIA BLUETOOTH

CORTINA BLACKOUT CINZA
CLARO DUBLADO LISO COM
VOIL FLAME - TRILHO SUÍÇO
3,00X2,68 (LxA)

MICROONDAS
ELETROLUX 20L
INOX ESPELHADO
COM FUNÇÃO TIRA
ODOR
**POR CONTA DO
CLIENTE**

COOKTOP DE INDUÇÃO
2 BOCAS
APLICADO NA HORIZONTAL

PURIFICADOR ELÉTRICO
COMPACTO ELECTROLUX
FILTRO REFIL TOUCH
BIVOLT GRAFITE
POR CONTA DO CLIENTE

FORNO E FRYER 25L
OSTER MULTIFUNÇÕES 10
EM 1 127V
POR CONTA DO CLIENTE

TV 55" SMART
PHILCO COM ROKU
POR CONTA DO CLIENTE
+
SUPORTE INCLUSO NO
ORÇAMENTO

CADEIRA EIFFEL WOOD
SOLO DESIGN
PRETO
02 UNIDADES

TODAS AS MEDIDAS DEVEM SER CONFERIDAS NO LOCAL E SÃO DE RESPONSÁBILIDADE DO FORNECEDOR CONTRATADO

RESPONSÁVEL TÉCNICO: ARQUITETO THIAGO DANTAS DO AMOR - CAU A162437-7

Bwild	EXECUTIVO	PROPRIETÁRIO: VICTOR GABRIEL PINTO GUEDES		CONTEÚDO: LISTAGEM COMPLEMENTOS	
		ARQUITETO: GUILHERME F.	DATA: 29/08/2025	REVISÃO: 03	FOLHA: 12/16

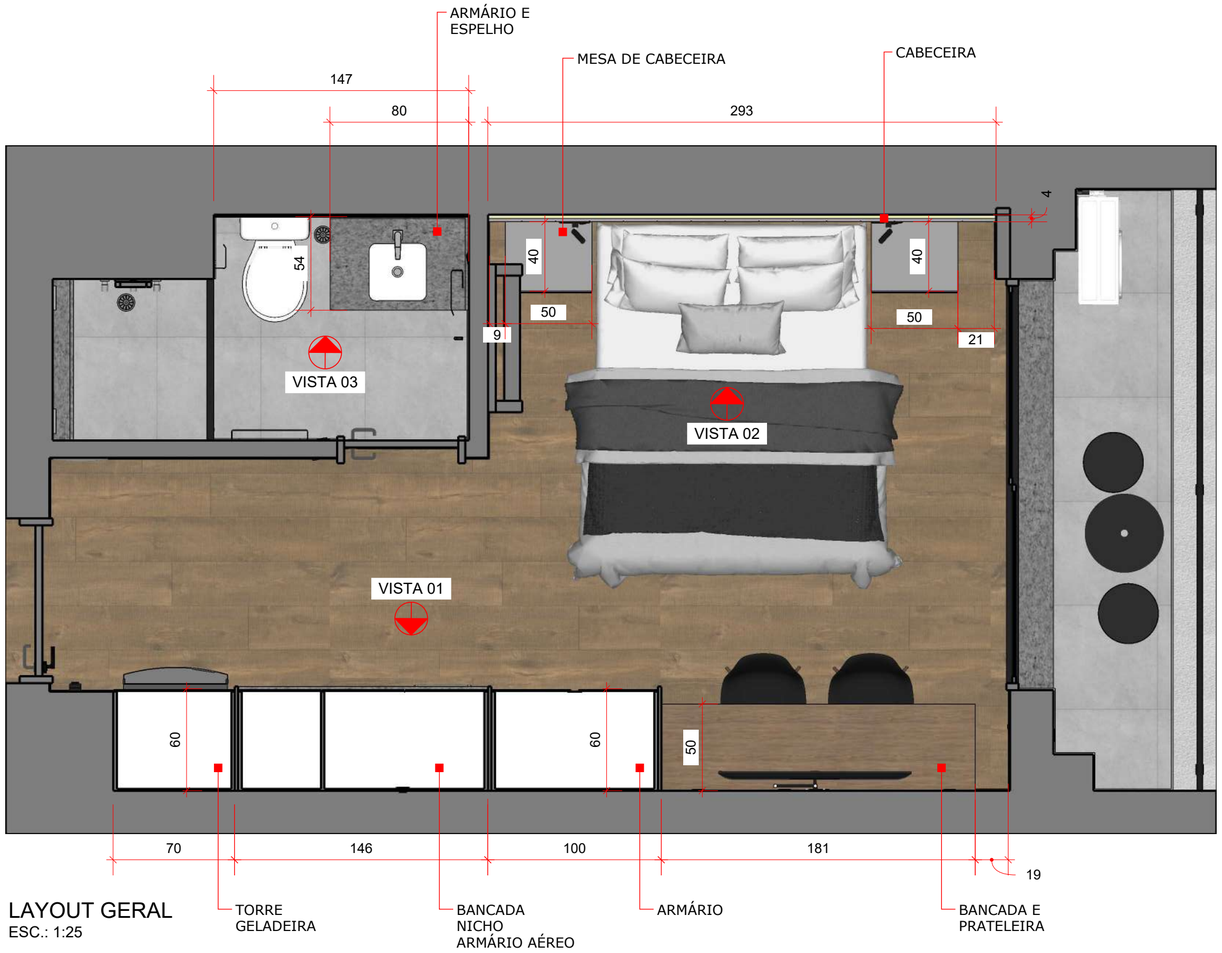

LAYOUT GERAL
ESC.: 1:25

LEGENDA:

MDF SAVANA
GUARARAPES

MDF CINZA
PERFEITO
GUARARAPES

MDF INTERNO
BRANCO
ÁRTICO

TODAS AS MEDIDAS DEVEM SER CONFERIDAS NO LOCAL E SÃO DE RESPONSÁBILIDADE DO FORNECEDOR CONTRATADO

RESPONSÁVEL TÉCNICO: ARQUITETO THIAGO DANTAS DO AMOR - CAU A162437-7

Bwild	EXECUTIVO	PROPRIETÁRIO: VICTOR GABRIEL PINTO GUEDES		CONTEÚDO: PLANTA MARCENARIA
		ARQUITETO: GUILHERME F.	DATA: 29/08/2025	REVISÃO: 03 / FOLHA: 13/16

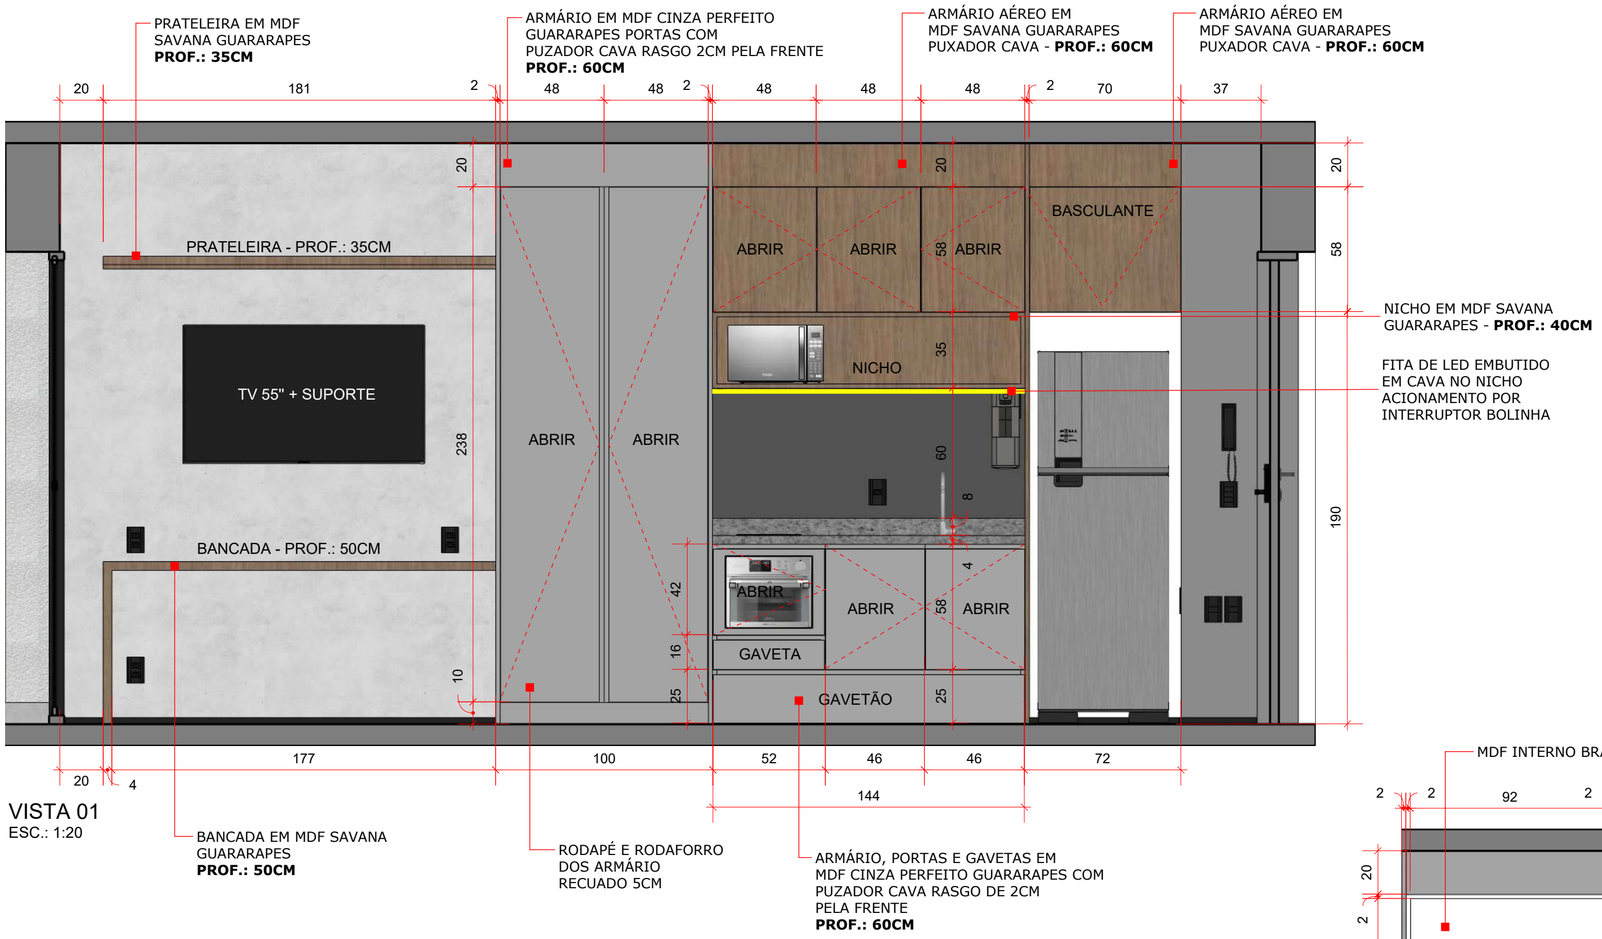

VISTA 01
ESC.: 1:20

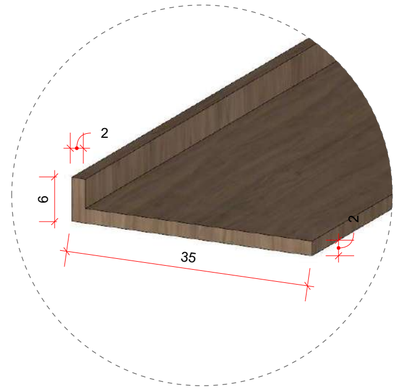

DET. 03 - PERSPECTIVA PRATELEIRA
ESC.: 1:5

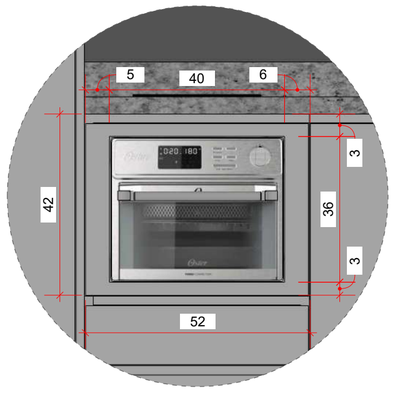

DET. 01 - DETALHE FRENTE FORNO E FRYER - ABERTURA POR FECHO TOQUE E CONFERIR MODELO ELETRO ANTES DA EXECUÇÃO

ESC.: 1:10

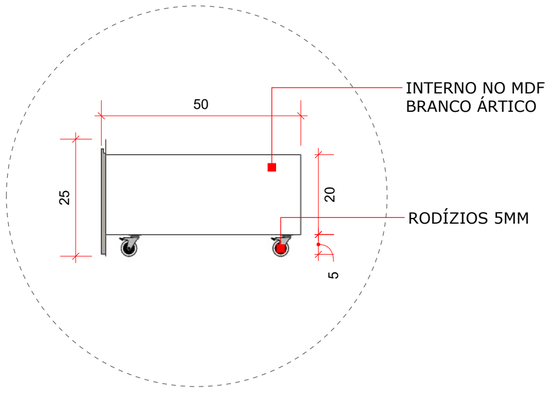

DET. 02 - VISTA LATERAL GAVETÃO
ESC.: 1:10

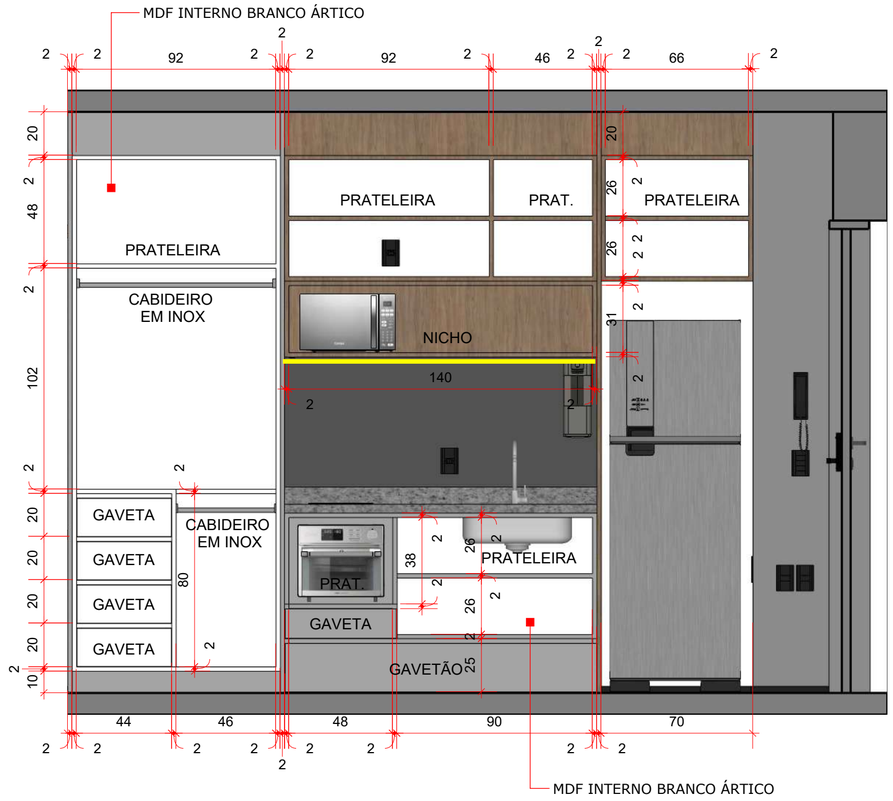

VISTA 01 - INTERNO
ESC.: 1:20

TODAS AS MEDIDAS DEVEM SER CONFERIDAS NO LOCAL E SÃO DE RESPONSÁBILIDADE DO FORNECEDOR CONTRATADO

RESPONSÁVEL TÉCNICO: ARQUITETO THIAGO DANTAS DO AMOR - CAU A162437-7

Bwild	EXECUTIVO	PROPRIETÁRIO: VICTOR GABRIEL PINTO GUEDES		CONTEÚDO: VISTAS MARCENARIA	
		ARQUITETO: GUILHERME F.	DATA: 29/08/2025	REVISÃO: 03	FOLHA: 14/16

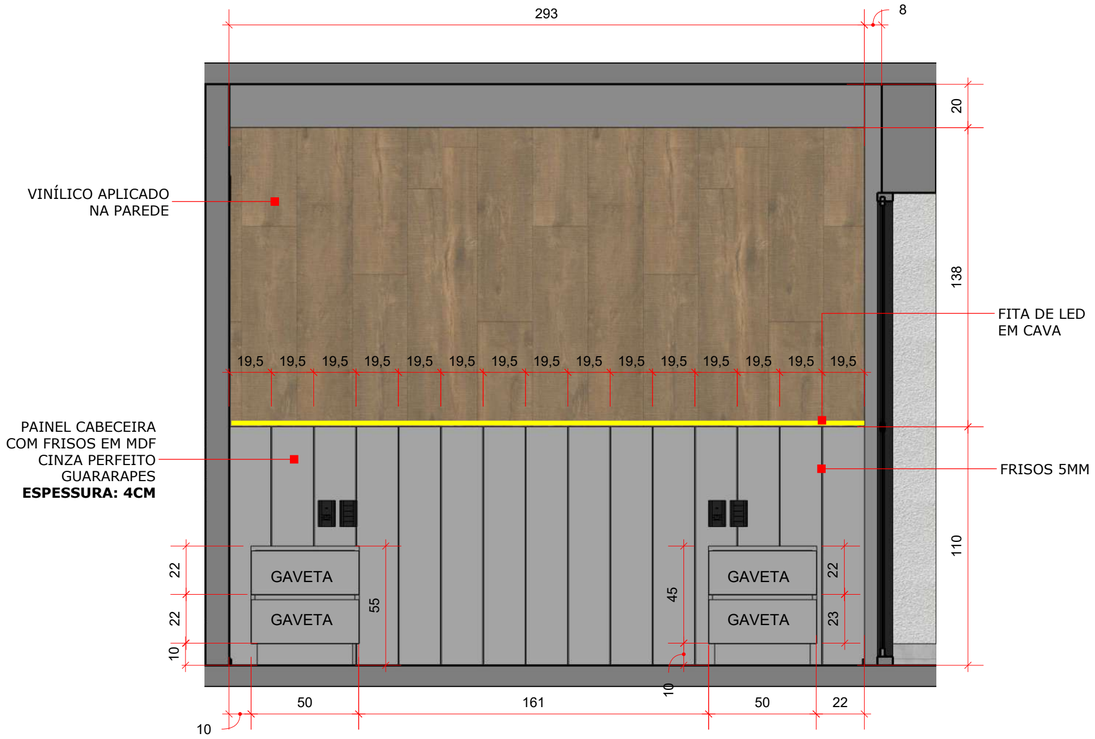

VISTA 02
ESC.: 1:20

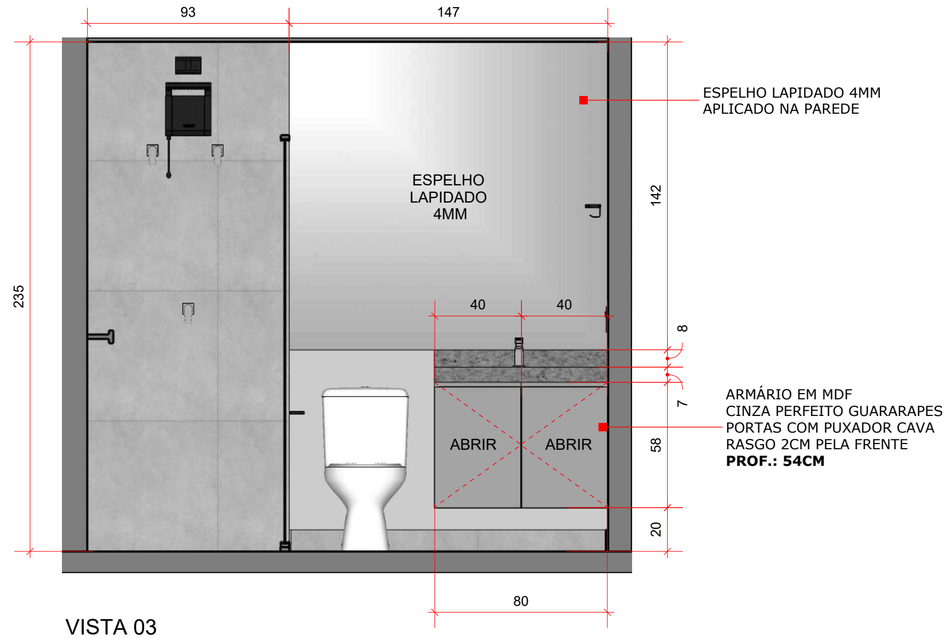

VISTA 03
ESC.: 1:20

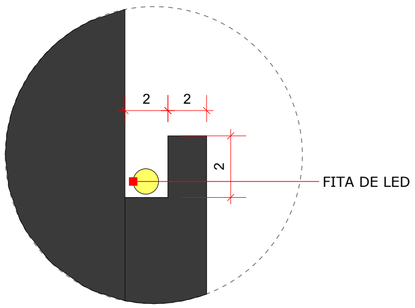

DET. 04 - FITA DE LED EM CAVA
ESC.: 1:5

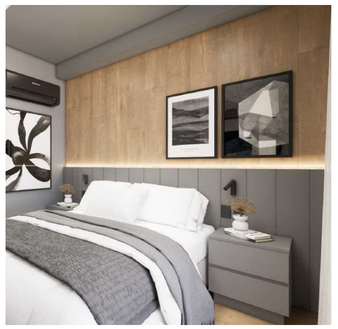

VISTA 03 - INTERNO
ESC.: 1:20

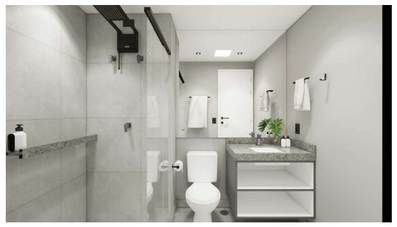

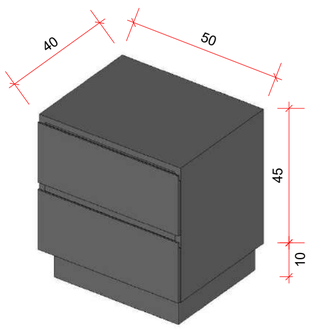

PERSPECTIVA MESA DE CABECEIRA

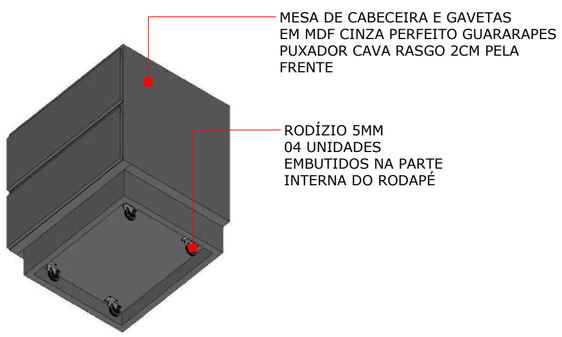

PERSPECTIVA INFERIOR MESA DE CABECEIRA

TODAS AS MEDIDAS DEVEM SER CONFERIDAS NO LOCAL E SÃO DE RESPONSÁBILIDADE DO FORNECEDOR CONTRATADO

RESPONSÁVEL TÉCNICO: ARQUITETO THIAGO DANTAS DO AMOR - CAU A162437-7

Bwild	EXECUTIVO	PROPRIETÁRIO: VICTOR GABRIEL PINTO GUEDES		CONTEÚDO: VISTAS MARCENARIA	
		ARQUITETO: GUILHERME F.	DATA: 29/08/2025	REVISÃO: 03	FOLHA: 15/16

TERMO DE APROVAÇÃO

EU, **VICTOR GABRIEL PINTO GUEDES,** APROVO ESTE PROJETO EXECUTIVO E CONCORDO COM TODAS AS ESPECIFICAÇÕES, DESENHOS E MEDIDAS INFORMADAS. PORTANTO, AUTORIZO O INÍCIO DA OBRA CONFORME ESTE PROJETO EXEUTIVO.

DATA: 29/08/2025